


PLAN SHOWING THE PROPOSED CONSTRUCTION OF RESIDENTIAL BUILDING AT PLOT NO.C-35,

AMBATTUR- ORAGADAM CO- OPERATIVE BUILDING SOCIETY'S COLONY, VIVEKANANDA NAGAR, THIRUMULLAIVOYAL,

AMBATTUR, CHENNAI - 600 053. COMPRISED IN S.NO.454/1B & 454/3 OF THIRUMULLAIVOYAL VILLAGE, AVADI TALUK,

THIRUVALLUR DISTRICT, AVADI CITY MUNICIPAL CORPORATION LIMIT.

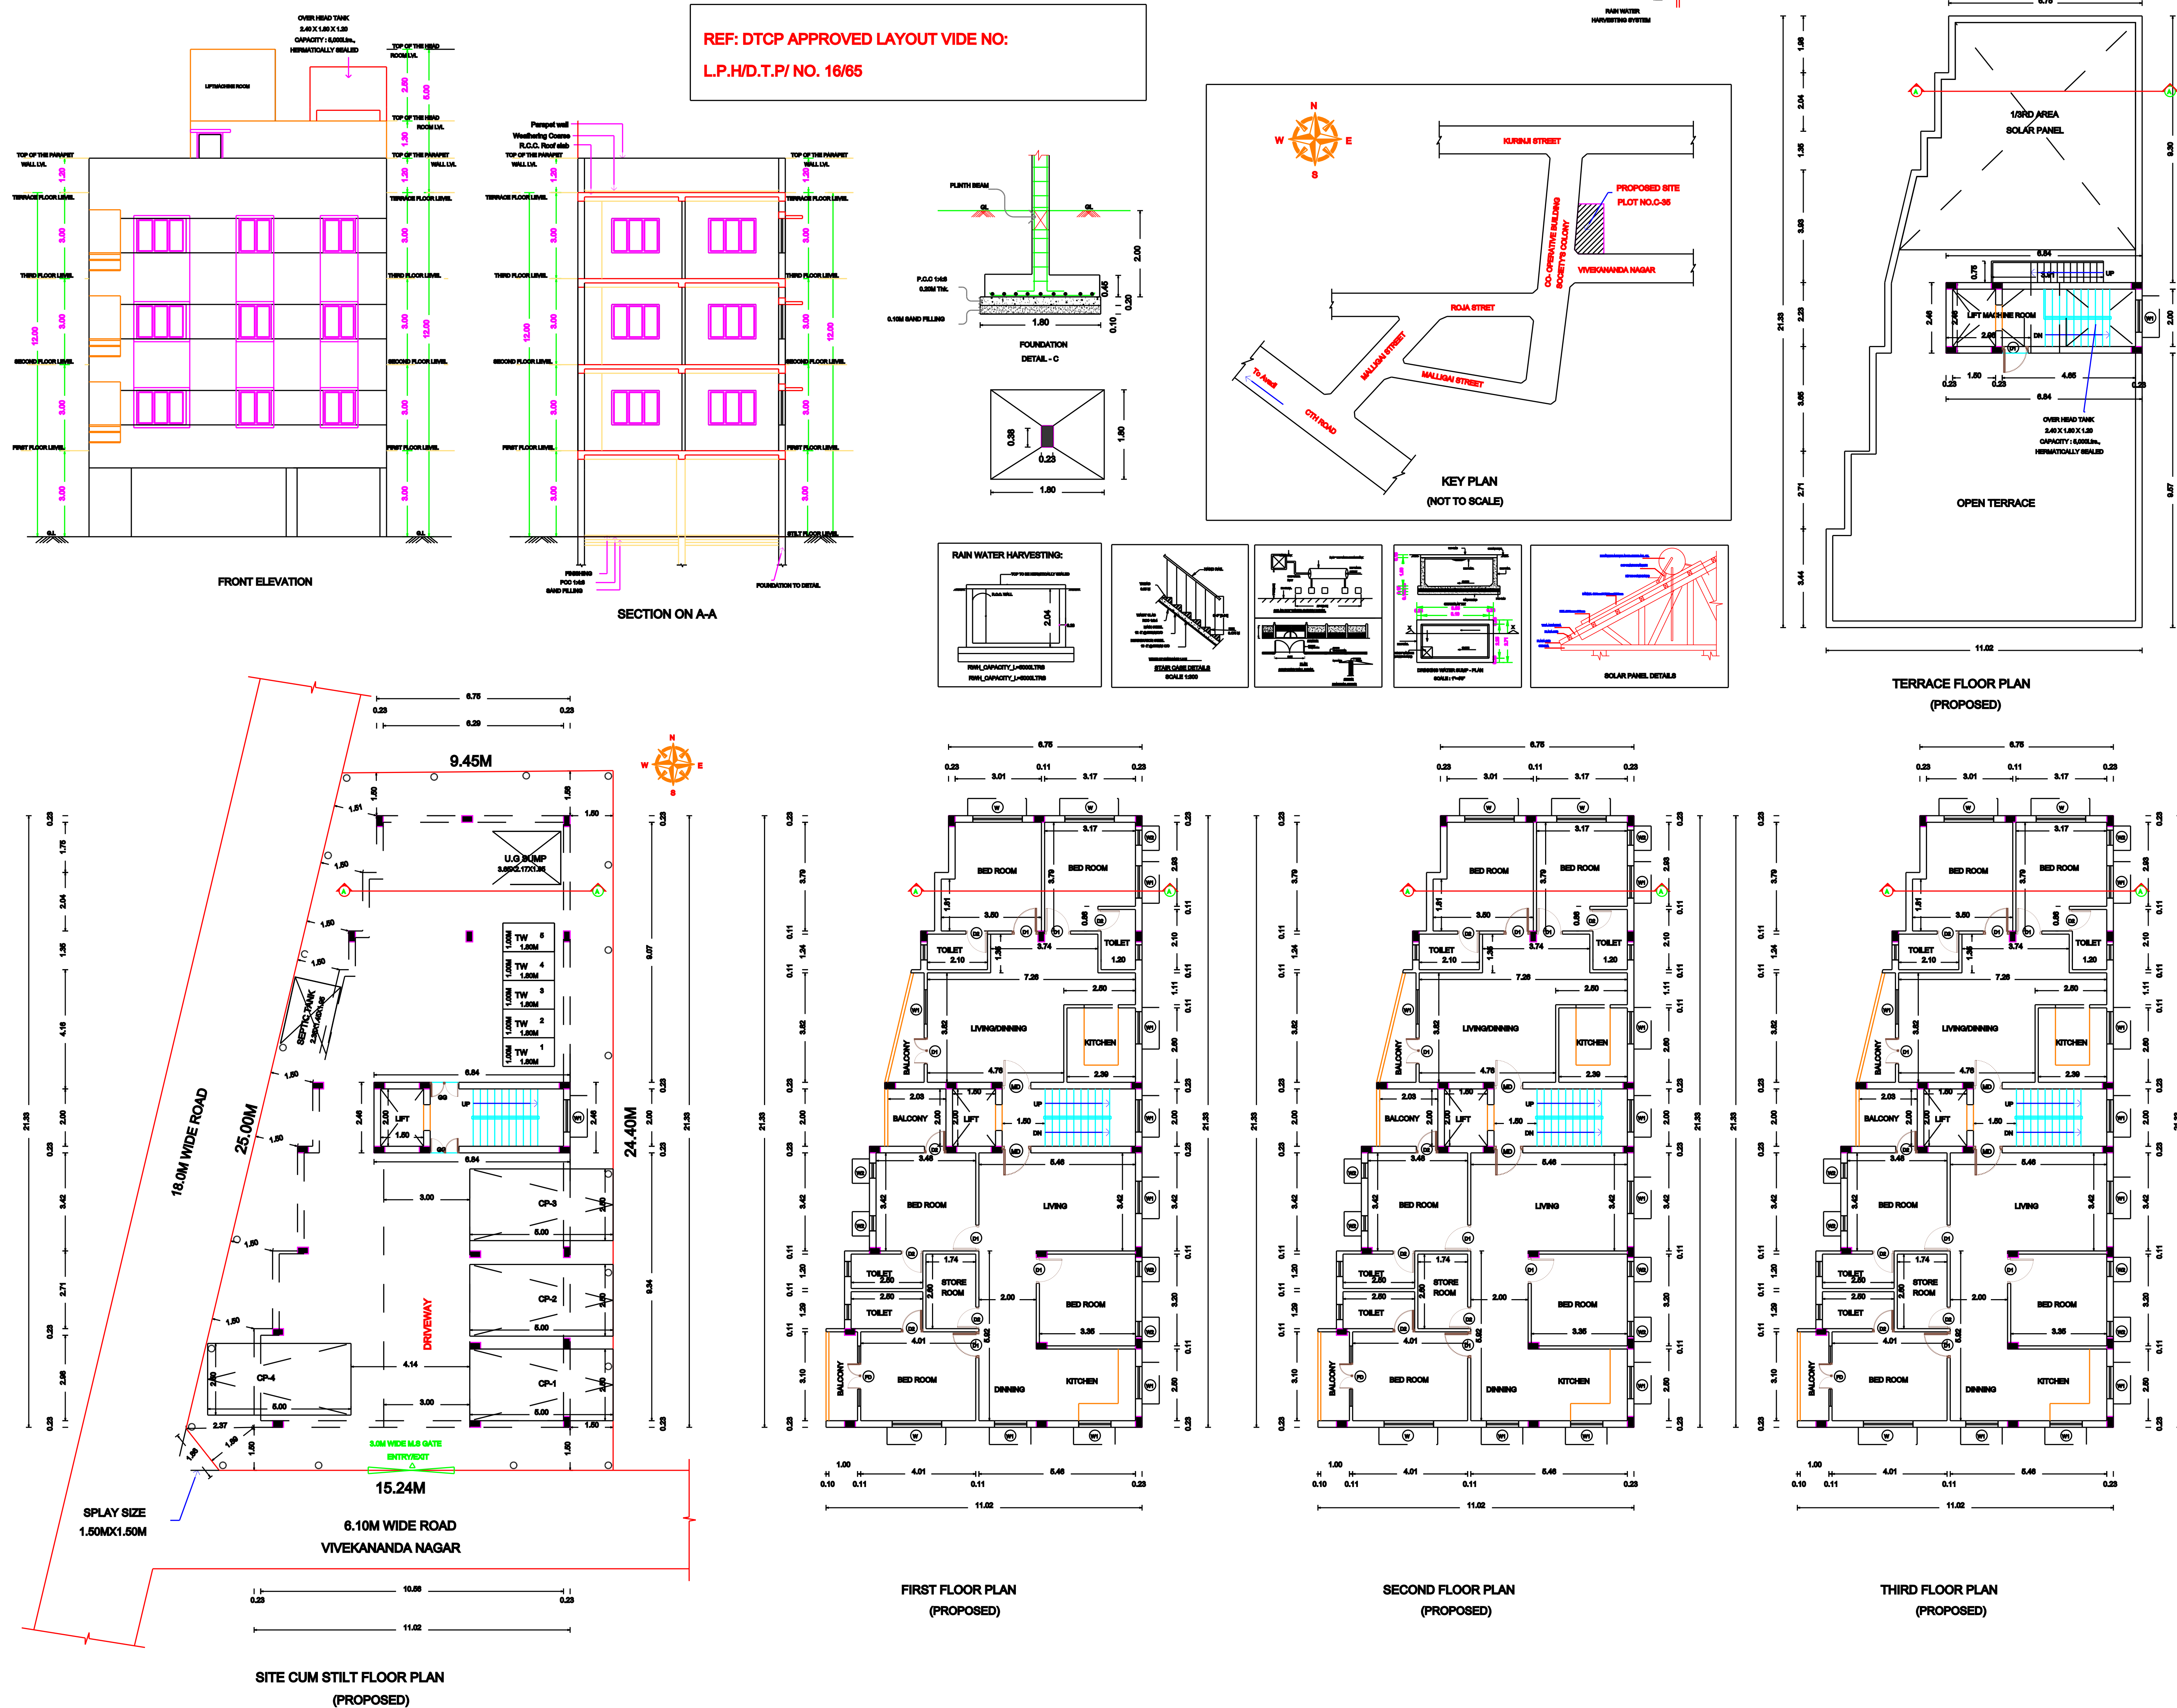

SCHEDULE OF JOINERY

MD	TEAK WOOD DOOR	1.00 X 2.13
D1	TEAK WOOD DOOR	0.90 X 2.13
D2	WATER PROOF FLUSH DOOR	0.75 X 2.13
W	TEAK WOOD WINDOW	1.80 X 1.20
W1	TEAK WOOD WINDOW	1.20 X 1.20
W2	TEAK WOOD WINDOW	0.80 X 1.50
FD	TEAK WOOD WINDOW	2.10 X 2.10
V1	VENTILATOR	0.80 X 0.80

AREA STATEMENT	AREA IN SQ.FT	AREA IN SQ.M
PLOT AREA (AS PER PATT)	3260.00	302.86
PLOT AREA (AS PER DOCUMENT)	3260.00	302.86
PLOT AREA (AS PER SITE)	3223.93	299.51
FSI AREA STATEMENT	F.S.I AREA (IN SQ. FT)	F.S.I AREA (IN SQ. M)
FIRST FLOOR	2074.44	192.72
SECOND FLOOR	2074.44	192.72
THIRD FLOOR	2074.44	192.72
TOTAL FSI AREA	6223.32	578.16
NON FSI AREA		
STILT PARKING	2074.44	192.72
HEAD ROOM	181.16	16.83
LIFT MACHINE ROOM	78.36	7.28
TOTAL FSI & NON FSI AREA	8557.28	794.99

FSI : 1.93

PLOT COVERAGE - 64.34%

NO OF DWELLING UNITS - 6 Nos

PARKING DETAILS	REQUIRED	PROVIDED
CAR	4 Nos	4 Nos
TWO WHEELER	2 Nos	5 Nos

COLOUR CODE

PROPOSED BUILDING	
EXISTING ROAD	
BOUNDARY LINE	

SPECIFICATIONS:

1. R.C.C ISOLATED FOOTINGS FOR FOUNDATIONS IN M20 MIX.
2. R.C.C COLUMNS IN M20 MIX.
3. R.C.C ROOF SLAB AND BEAMS IN M20 MIX.
4. 9" BRICK WORK IN C.M 1:5 IN SUPER STRUCTURE.
5. COUNTRY WOOD DOORS WITH FLUSH SHUTTERS.
6. COUNTRY WOOD GLAZED WINDOWS.
7. INTERNAL PLASTERING IN C.M 1:4.
8. EXTERNAL PLASTERING IN C.M 1:5.
9. WEATHERING COURSE IN BRICK JELLY LIME CONCRETE 1:3 MIX.
10. WEATHERING TILES IN 9"x9" BURNT CLAY TILES IN LAID IN 1:3 MIX.

OWNER SIGNATURE:

REGISTERED ENGINEER: