


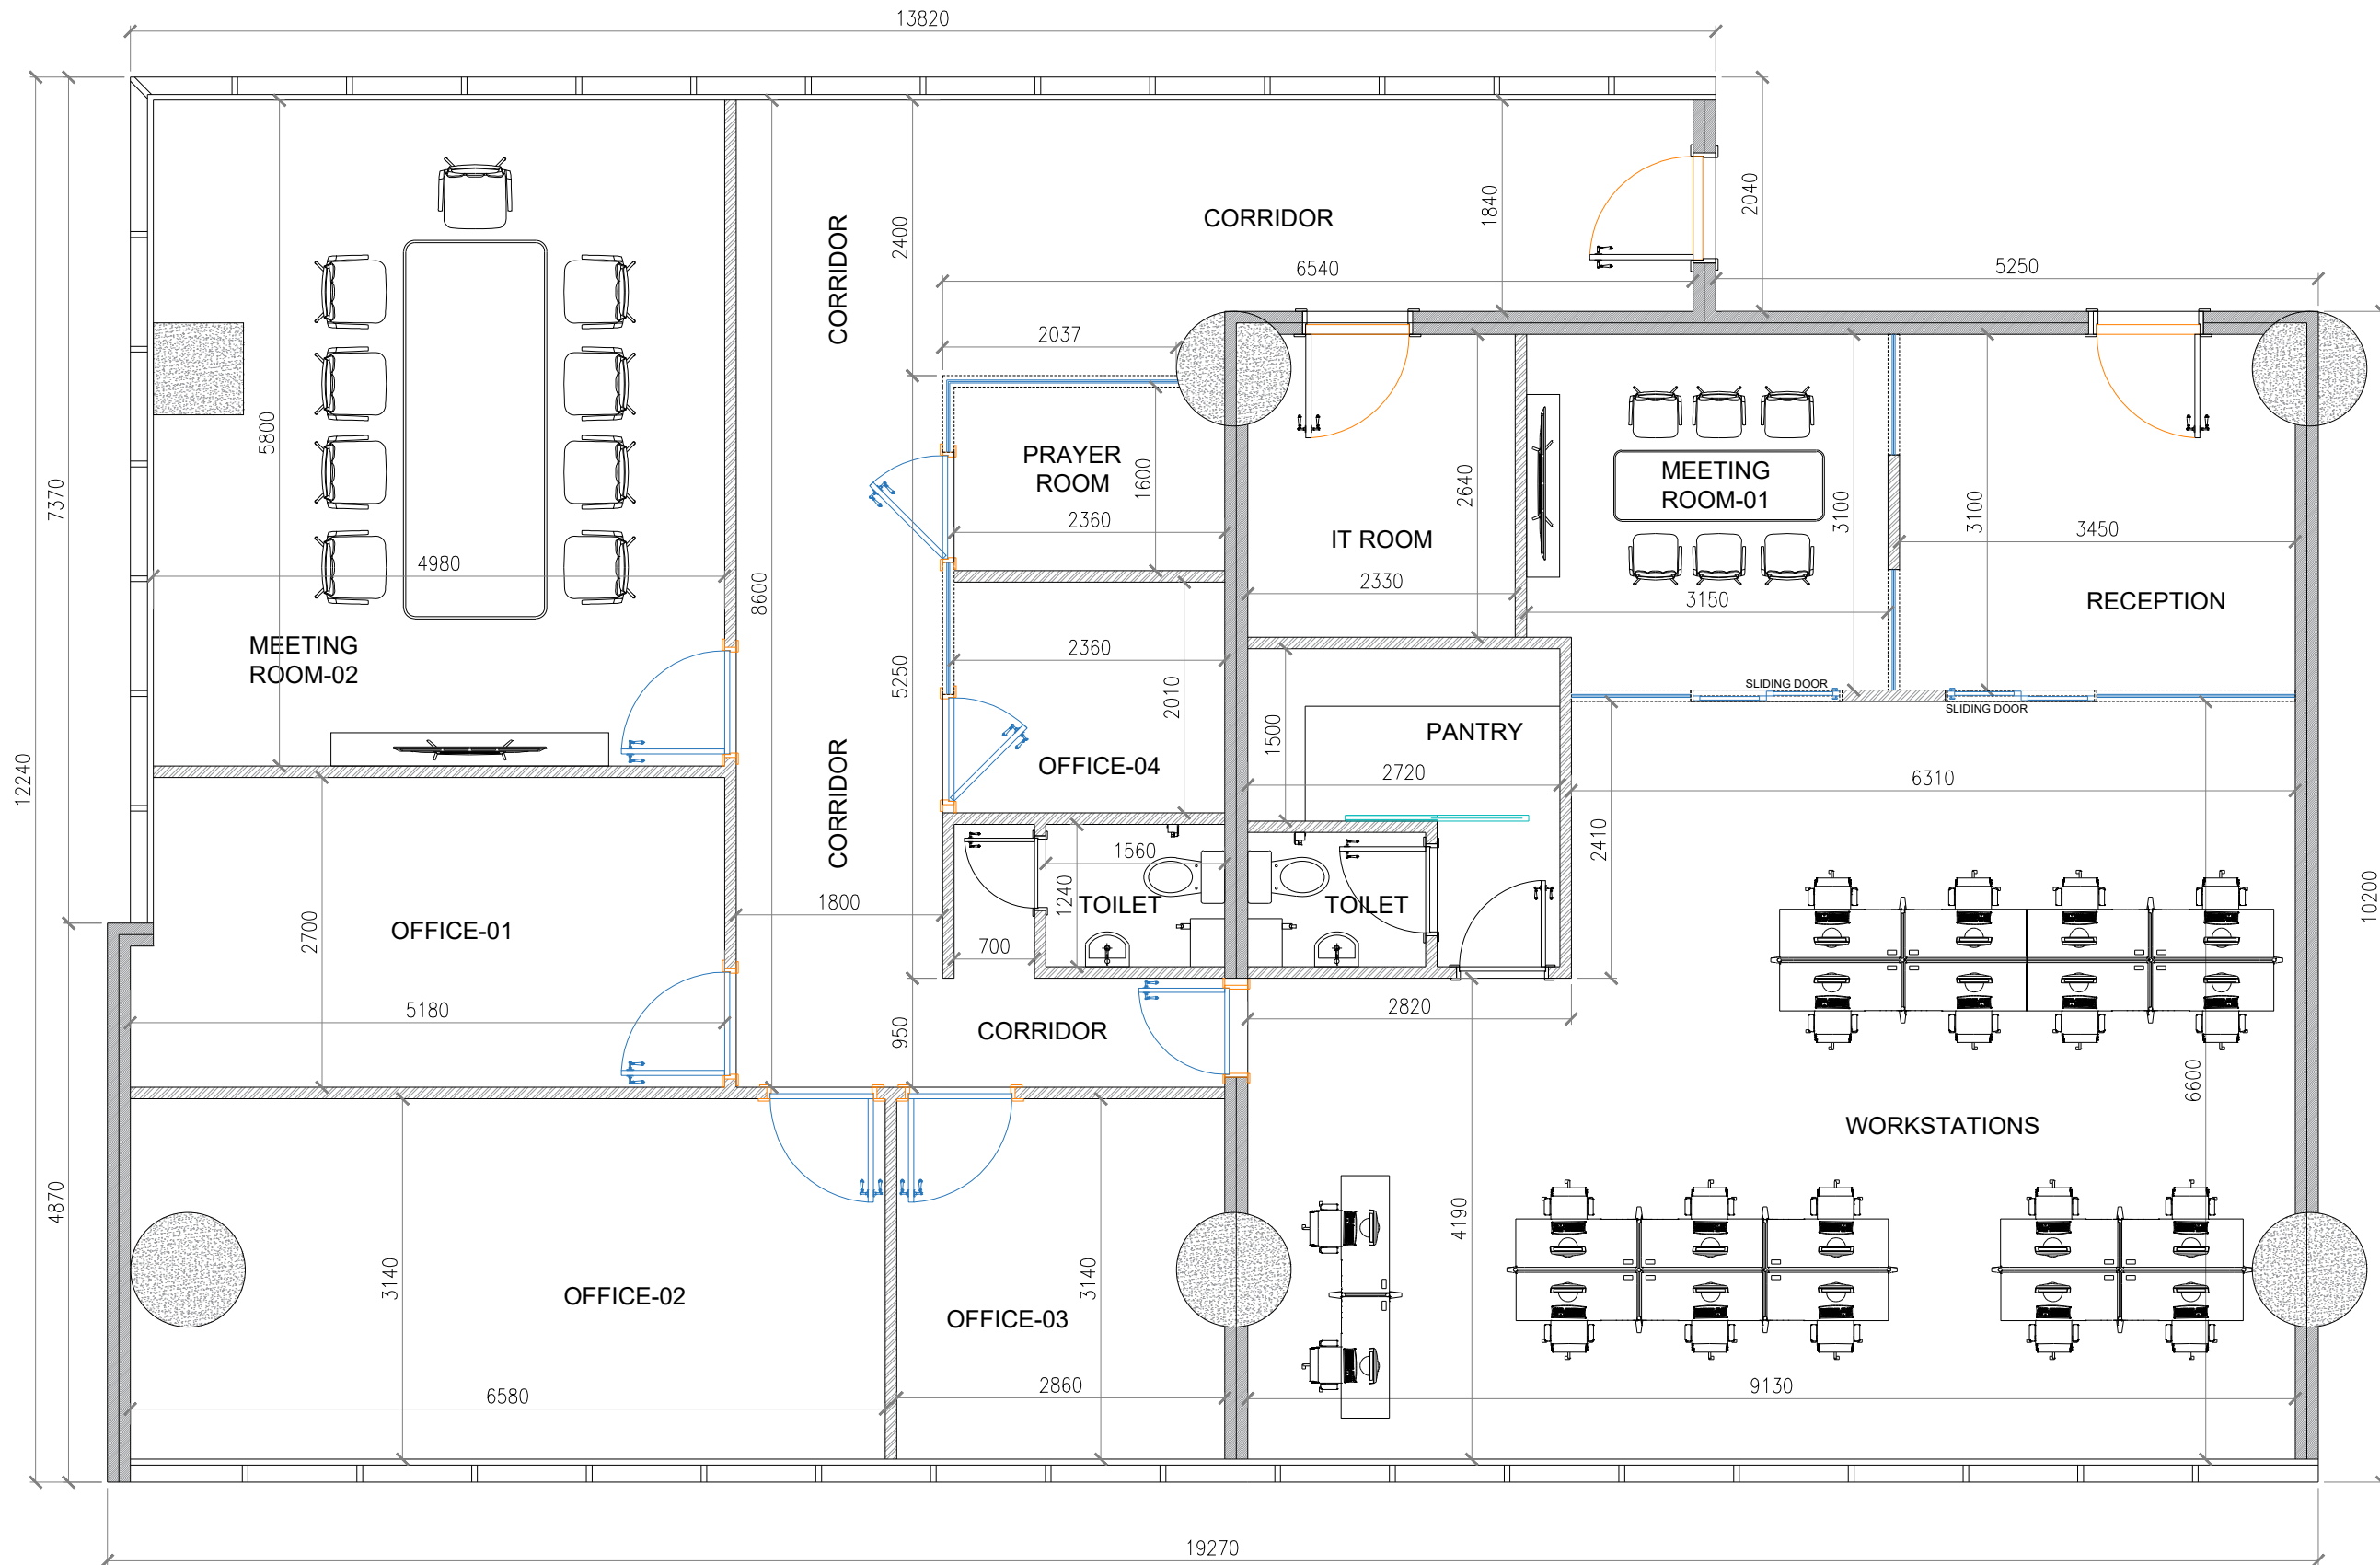

PROPOSED FLOOR LAYOUT

SCALE

1:100

LEGENDS

	EXISTING CONCRETE WALL
	PURPOSED GI WALL
	PROPOSED GLASS PARTITION

KEY PLAN

DOCUMENT REVIEW STATUS

- ☐ **CODE 1 - NO OBJECTION**
No objection - work may proceed.
- ☐ **CODE 2 - PROCEED AND RESUBMIT**
Proceed, revise and resubmit - work may proceed subject to incorporation of comments indicated.
- ☐ **CODE 3 - REJECTED**
Rejected, document not accepted - work may not proceed - revise and resubmit.
- ☐ **CODE 4 - REVIEW NOT REQUIRED**
Review not required - work may proceed.

Permission to proceed shall not relieve the supplier of all responsibility concerning submitted design details, shop drawings, calculations, method statements, project analysis, test methods or materials and from full compliance with the project and end user requirements.

Representative for/and on behalf of
Dubai Silicon Oasis Authority (DSOA) Date

NOTE & LEGENDS:

- DO NOT SCALE FROM THE DRAWINGS.
- ALL DIMENSIONS AND LEVELS ARE IN MILLIMETERS UNLESS NOTED OTHERWISE. ALL DIMENSIONS TO BE VERIFIED ON SITE & APPROVED BY ENGINEER.
- ALL MATERIAL SHOULD BE FIRE-RATED

*REVISION :

NO	DATE	FOR APPROVAL	REVISOR	REMARK
06				
05				
04				
03				
02				
01	12.05.2026			

PROJECT :-

OFFICE- 510 & 511
RENOVATION WORK

SHEET CONTENT :-

PROPOSED FLOOR LAYOUT

LOCATION:

SILICON OASIS DUBAI, UAE

CLIENT:



MAIN CONTRACTOR:



PREPARED BY: Hassan Nawaz	
DRAWING NO.: PR-OFF-AR-001	
DATE: 12.05.2026	SCALE: 1:100
CHECKED BY: GK	APPROVED BY: SS
REVISED NO.: 00	AUTHORIZED BY: